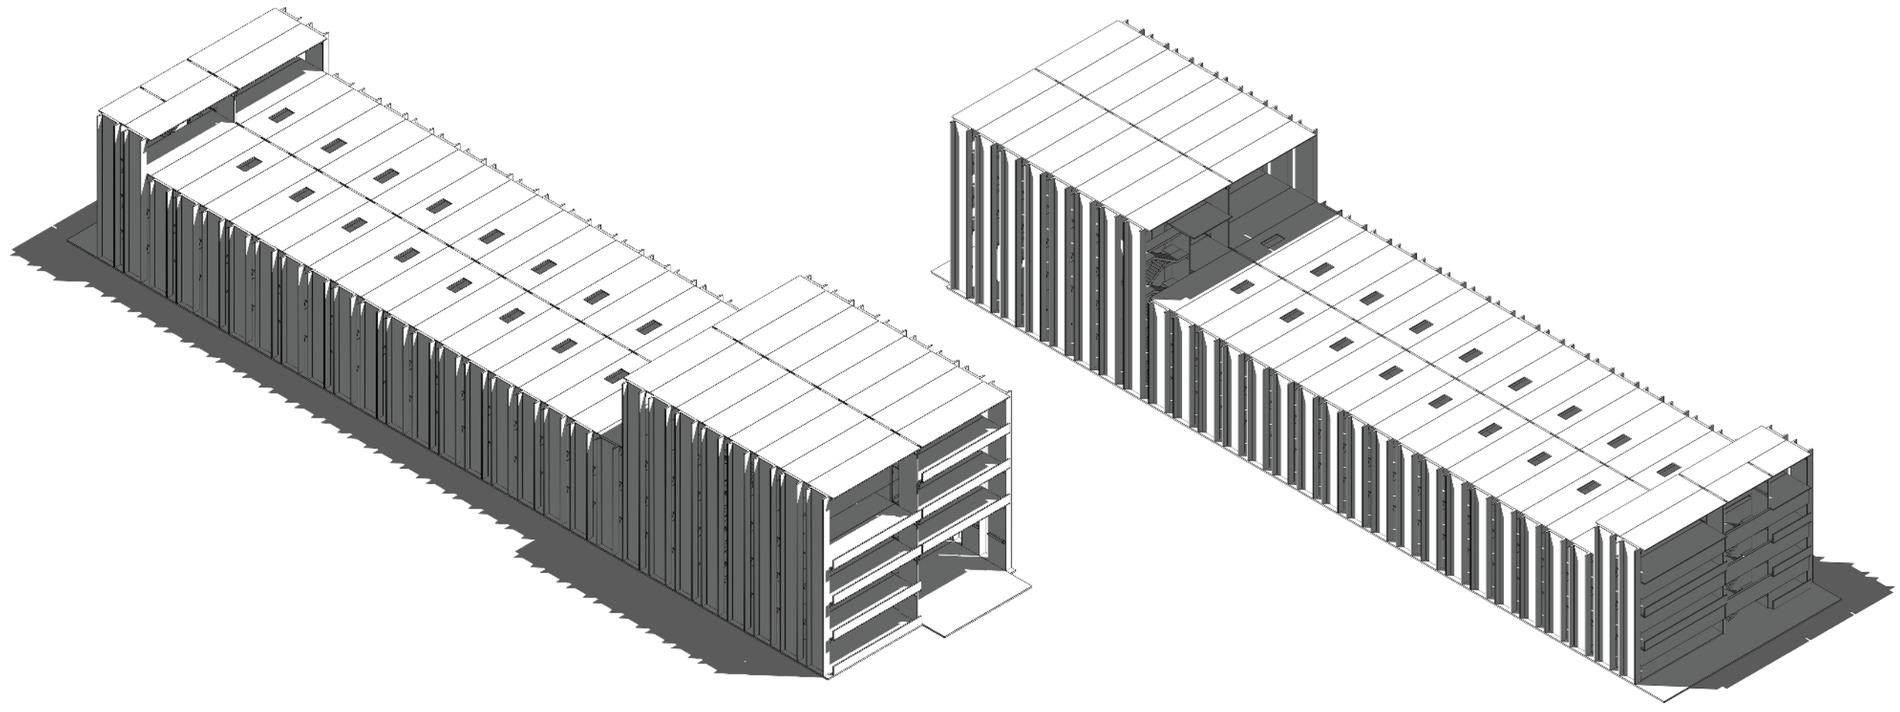


ALPHA
TYPE

A.3
VARIANT

VIRTUES

Alpha explores a variation on the traditional precast bearing wall and double-tee paradigm. Gap spaces between internal and external bearing wall panels create a rhythm of closed and open in an infinite sequence. Horizontal double-tee floor structure spans forty feet, with each stem resting on a sculptural haunch that expresses the muscular transfer of load.

The building form rises or falls depending on single or double floor height. The enclosed space rises and falls with the form and extends expansively in the long-grain direction, with lateral passageways expressed every twelve feet.

Enclosure on the long east and west sides is comprised of structural insulated panels. They are course in texture and oriented with a strong vertical bias. Vertical fins project out beyond the glazing apertures to minimize solar gain while creating dynamic shadow play.

Enclosure on the short north and south sides has a horizontal bias created by deeply-recessed insulated spandrel panels and projecting guardrail panels. Glazing is held back from the facade, while maximizing transparency. The main entry is on the south and a protected service dock is on the north.

MEASURES

Building Footprint
80 feet by 336 feet = 26,880 square feet


Structural Bay Size
12 feet by 40 feet
40 foot wide by infinity column-free space


Building Height
14 foot and 28 foot floor-to-floor height
Three stories at 42 feet to 70 feet total height

Area of Precast Elements
129,080 square feet of structure and enclosure


Enclosure Glazing Ratio
22% of total thermal enclosure




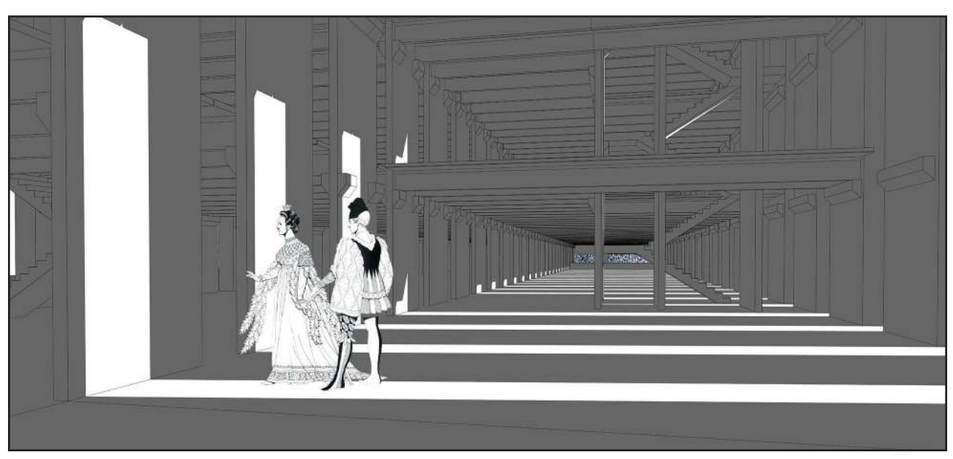


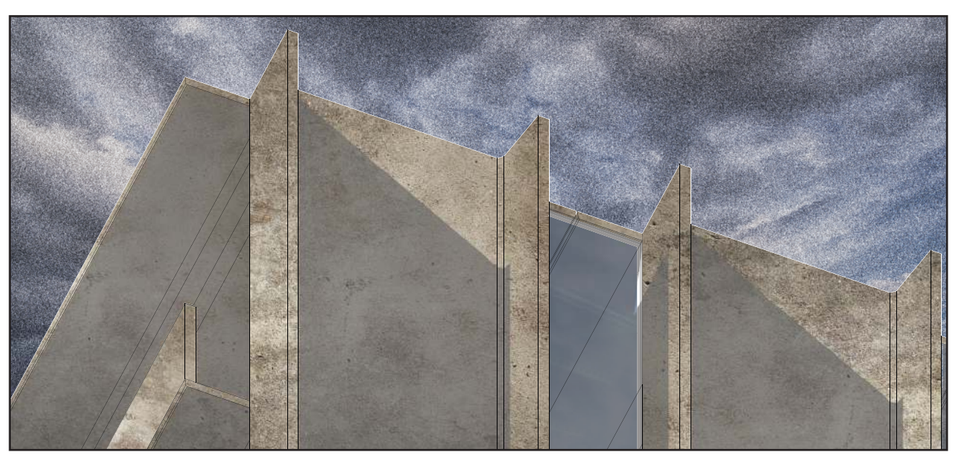



FINITE ELEMENTS

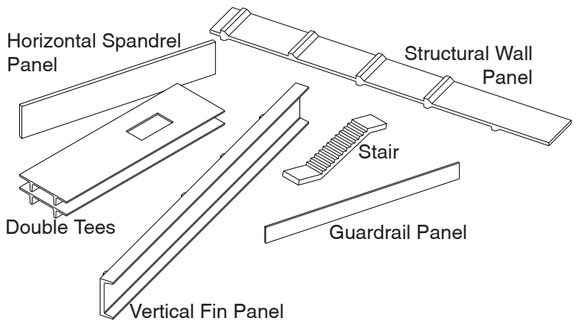

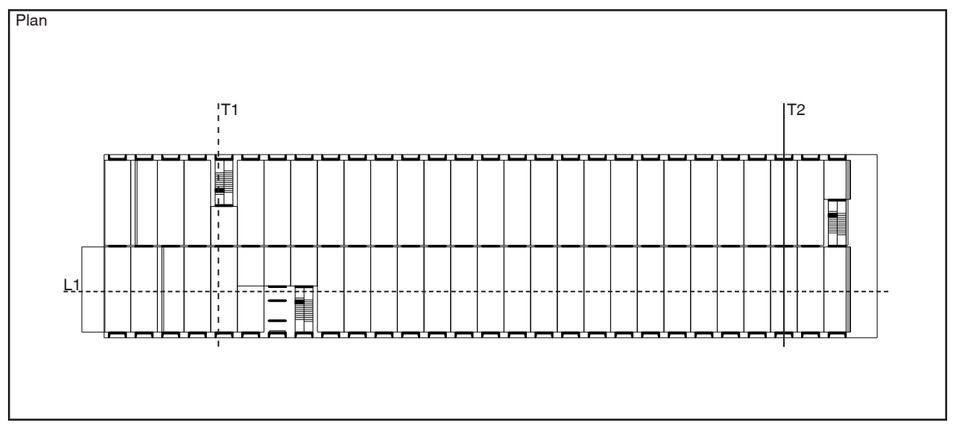

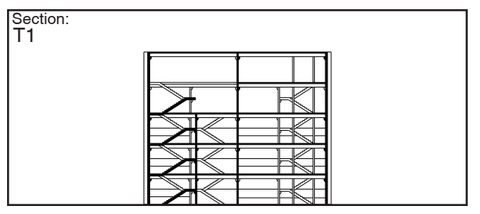

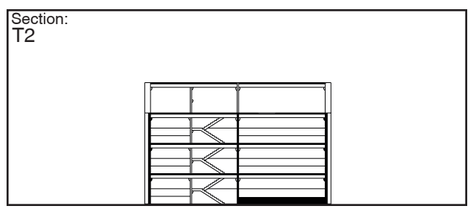

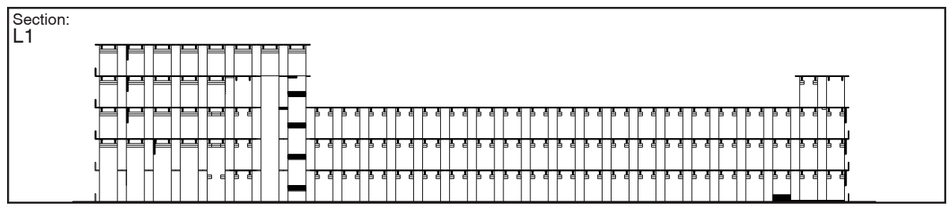

PRECAST
PROTOTYPES

