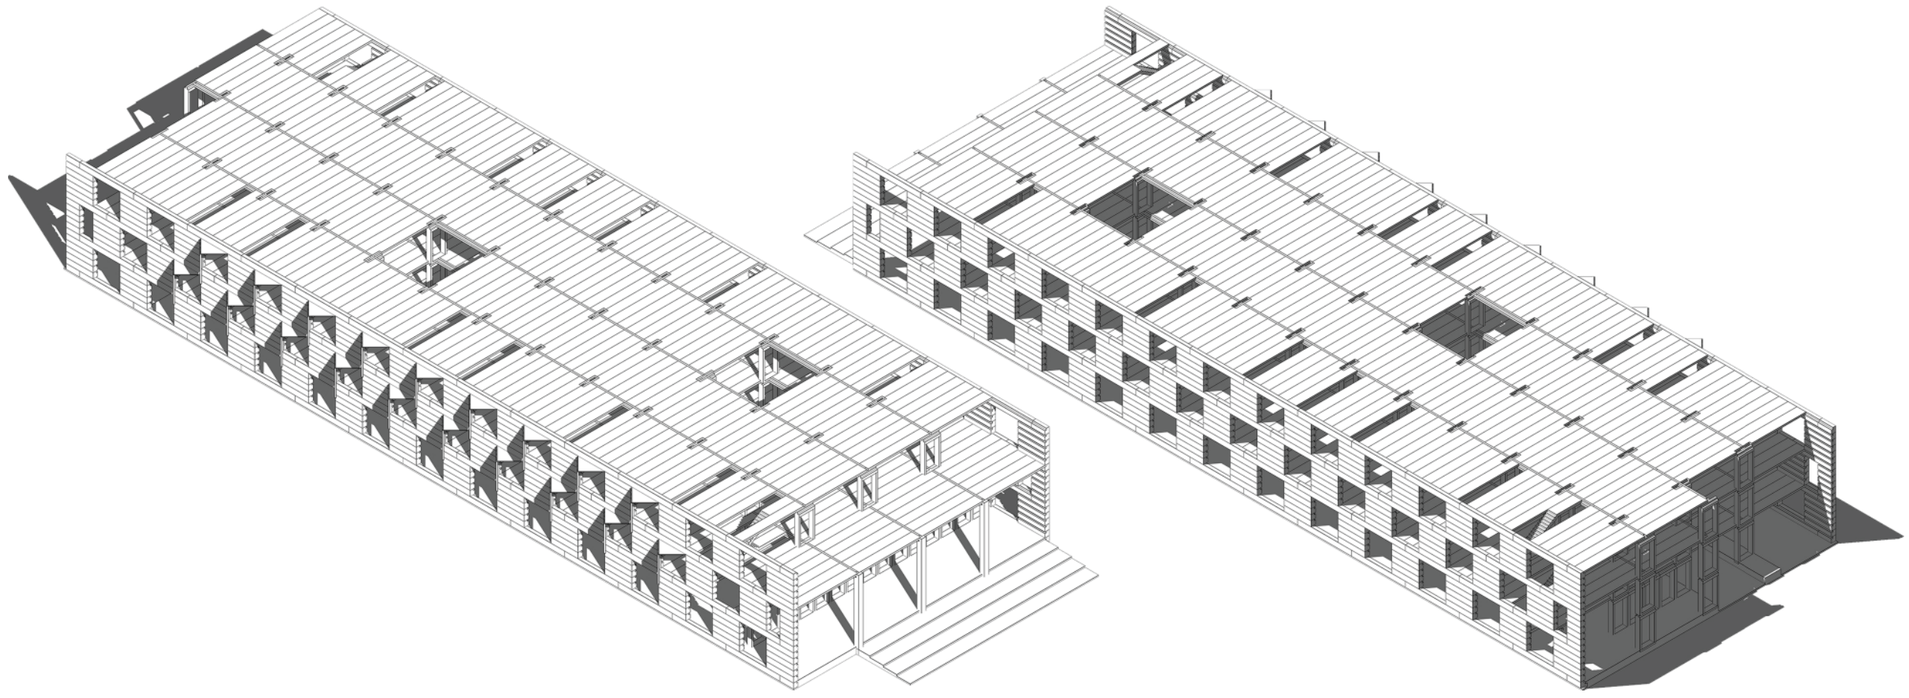


KILO
TYPE

K.3
VARIANT

VIRTUES

Kilo explores the expressive potential of cyclopean precast blocks, commonly called “waste blocks” in the precast industry. They are cast in formwork utilizing the leftover wet concrete from wall panel or double-tee casting. Their weight and mass act as monumental bearing walls requiring no additional reinforcement.

Floors and roof are defined by hollow-core planks spanning twenty-eight feet. The plank spans between perimeter bearing walls and interior beams. The beams span between lite walls every twenty-four feet that function like columns with built-in portals to define circulation paths within the building.

Enclosure on the long east and west sides is comprised of the insulated cyclopean blocks that create openings for transparent glazing. Precast screen hoods shield the openings and minimize direct solar gain while creating dramatic light and shadow effects.


Enclosure on the short north and south sides is composed with transparent and translucent glazing synchronized with the rhythm of the lite walls. A deep porch on the south side defines the main entry and provides shelter and transition between inside and out.

MEASURES


Building Footprint
114 feet by 324 feet = 36,936 square feet
Structural Bay Size
24 feet by 28 feet
24-foot wide column-free space
Building Height
14-foot floor-to-floor height
Three stories at 42 feet total height
Area of Precast Elements
126,416 square feet of structure and enclosure
Enclosure Glazing Ratio
50% of total thermal enclosure





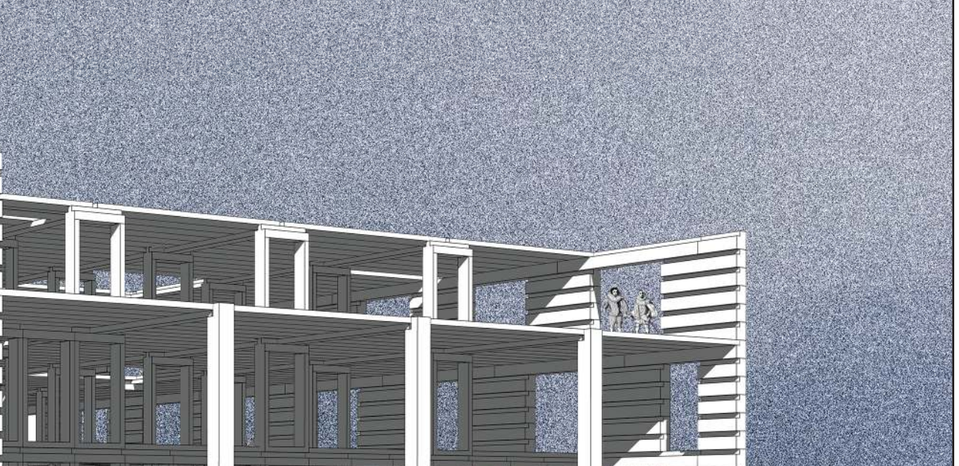

FINITE ELEMENTS

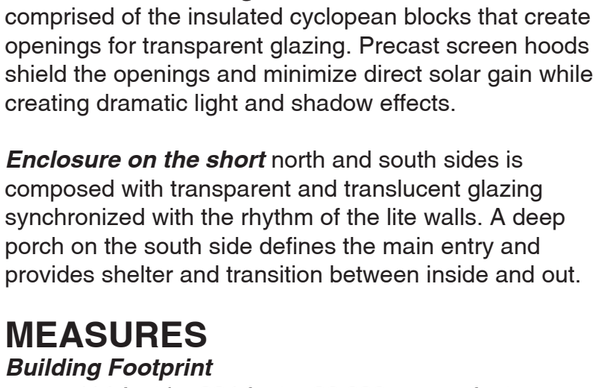

PRECAST
PROTOTYPES



